
Site plan

Rua Marquês de Paranaguá 111 (west) to Rua Caio Prado (east). Edifícios 01–04, auditorium, court, gardens, neighbours.

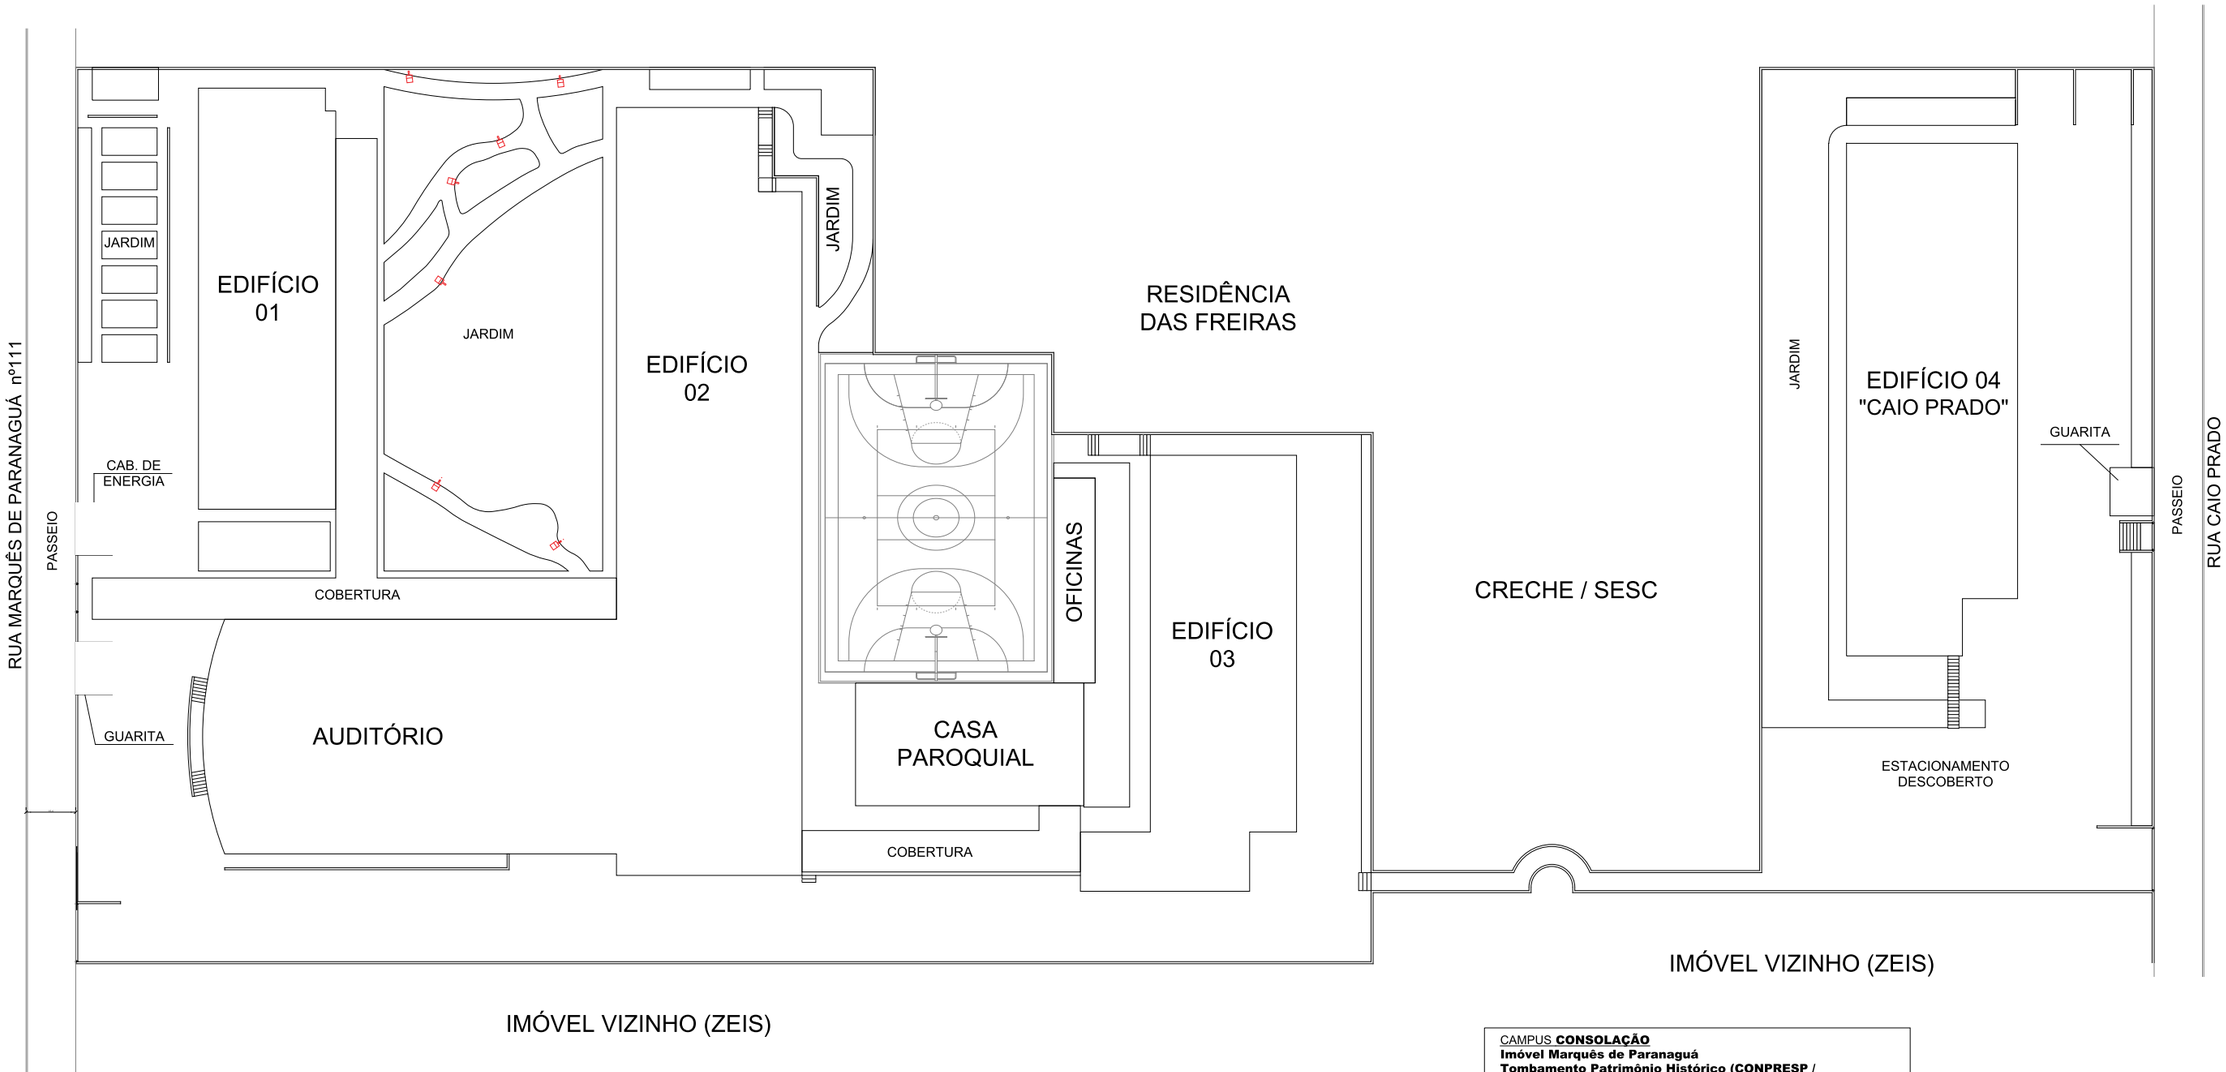


CAMPUS **CONSOLAÇÃO**
Imóvel Marquês de Paranaguá
Tombamento Patrimônio Histórico (CONPRESP / CONDEPHAAT)
- POPULAÇÃO FLUTUANTE TOTAL - 1600 alunos (em 26/09/2014)
- 20 SALAS DE AULA
- 04 AUDITÓRIOS
- 20 LABORATÓRIOS DE INFORMÁTICA
- LABORATÓRIOS TÉCNICOS

0 m — 20 m

Source: FUNDASP DIPLAD, MPCA_ARQ_Campus Marques_2024.11.06.dwg (sheets dated 25/11/2024). Converted with LibreDWG 0.14, rendered with ezdxf. Drawing units: metres.

Edifício 01


Ground, 1st and 2nd floors. Departments, coordinations, SAE, teachers' room, labs, postgraduate offices.

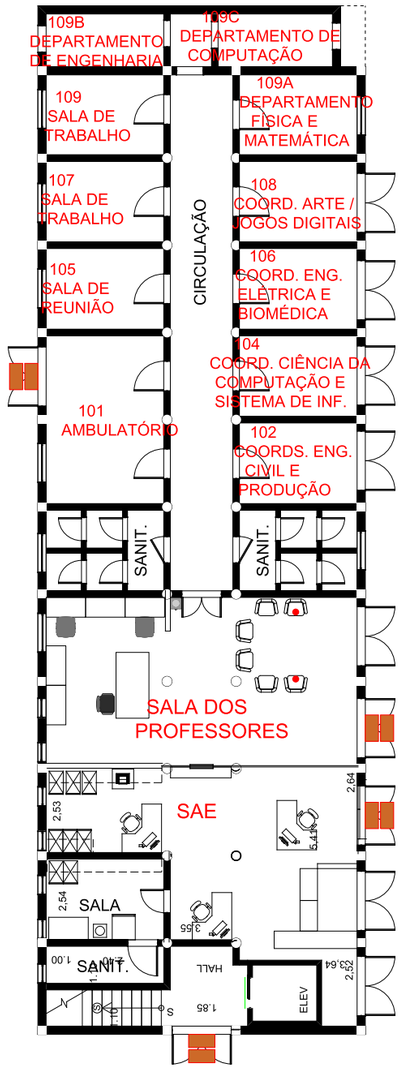

EDIFÍCIO 01 - TÉRREO
PLANTA BAIXA
ESC.: 1 / 200



EDIFÍCIO 01 - 1º ANDAR
PLANTA BAIXA
ESC.: 1 / 200

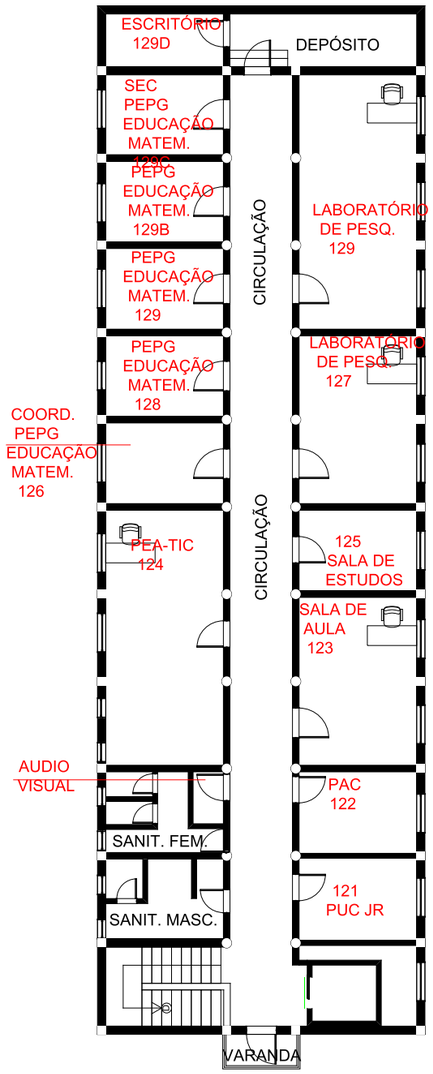


EDIFÍCIO 01 - 2º ANDAR
PLANTA BAIXA
ESC.: 1 / 200


0 m 5 m

Edifício 02


Basement (library, canteen), ground (auditorium, chapel, classrooms), 1st (direction, IT labs), 2nd (engineering labs). Fills mark room use: robotics lab (green), chapel (magenta), IT labs (grey).

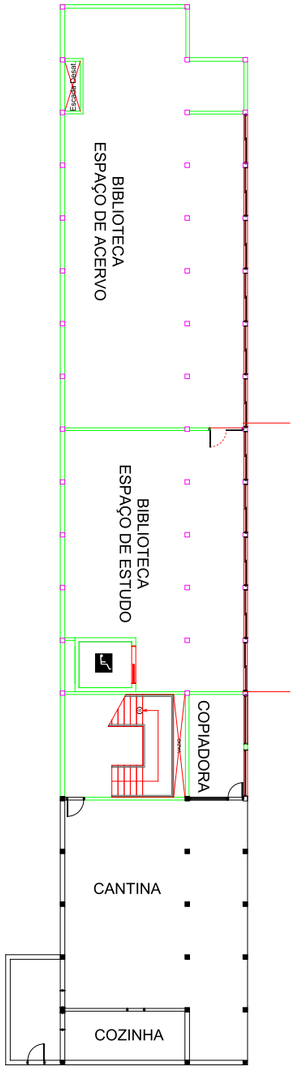


EDIFÍCIO 02 - SUBSOLO
PLANTA BAIXA
ESCALA: 1 / 300

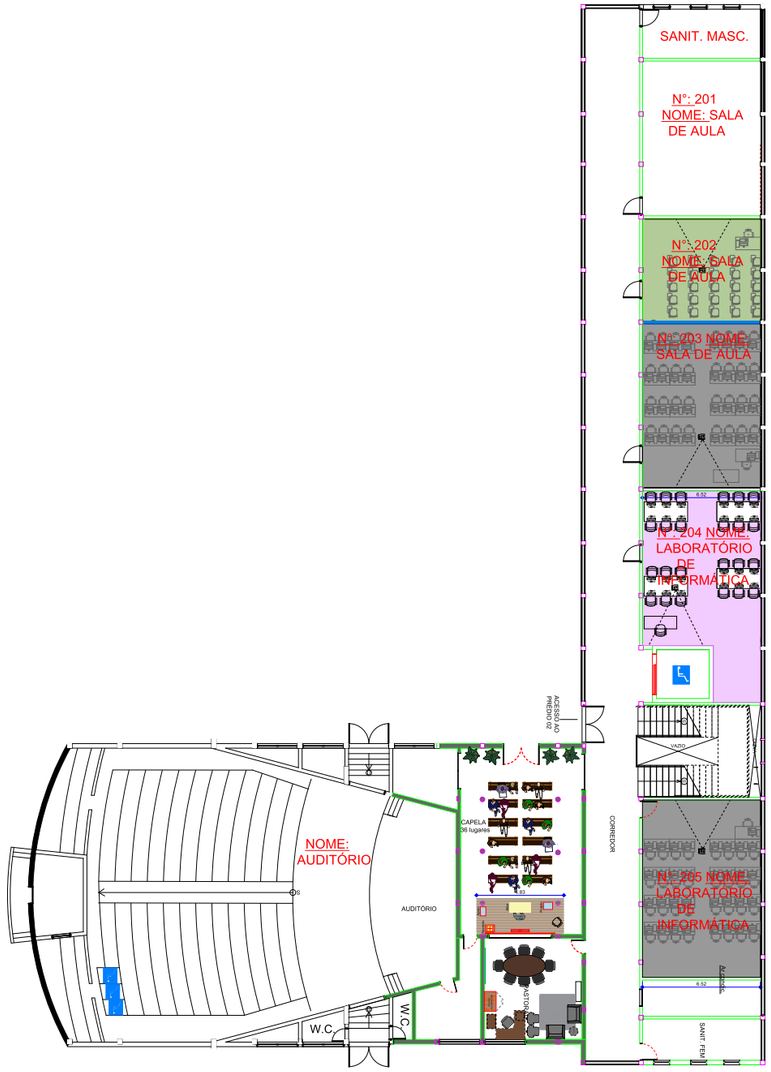

EDIFÍCIO 02 - TÉRREO
PLANTA BAIXA
ESCALA: 1 / 300

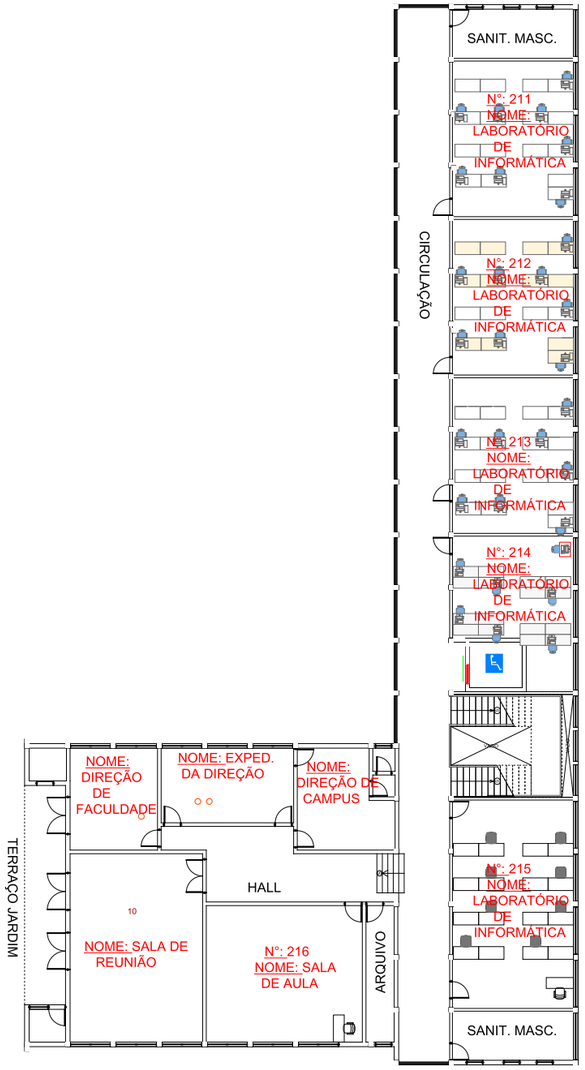

EDIFÍCIO 02 - 1º ANDAR
PLANTA BAIXA
ESCALA: 1 / 300

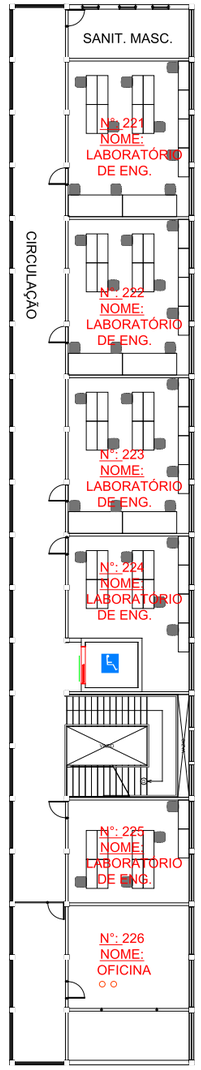


EDIFÍCIO 02 - 2º ANDAR
PLANTA BAIXA
ESCALA: 1 / 300

0 m 10 m


Source: FUNDASP DIPLAD, MPCA_ARQ_Campus Marques_2024.11.06.dwg (sheets dated 25/11/2024). Converted with LibreDWG 0.14, rendered with ezdxf. Drawing units: metres.

Edifício 03


Basement (mechanics/fluids labs, data centre; proposed layout) and three classroom floors (311–313, 321–323, 330–331).

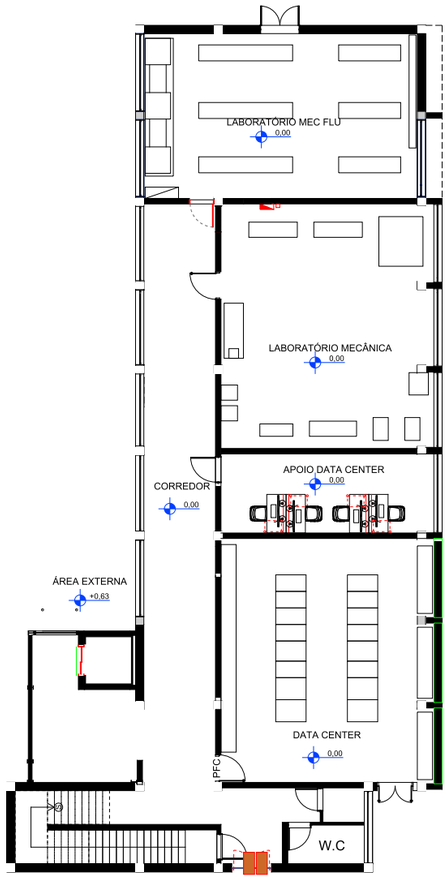


EDIFÍCIO 03 - SUBSOLO
PLANTA BAIXA - LAYOUT PROPOSTO
ESC.: 1 / 200

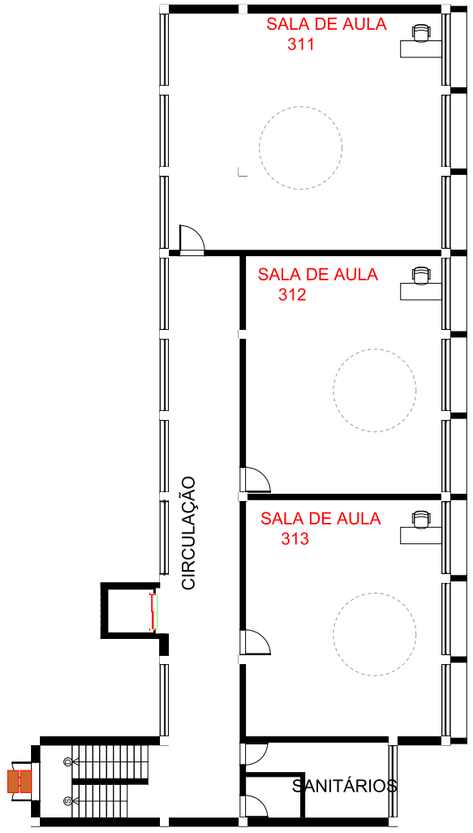

EDIFÍCIO 03 - 1º PAVIMENTO
PLANTA BAIXA
ESC.: 1 / 200

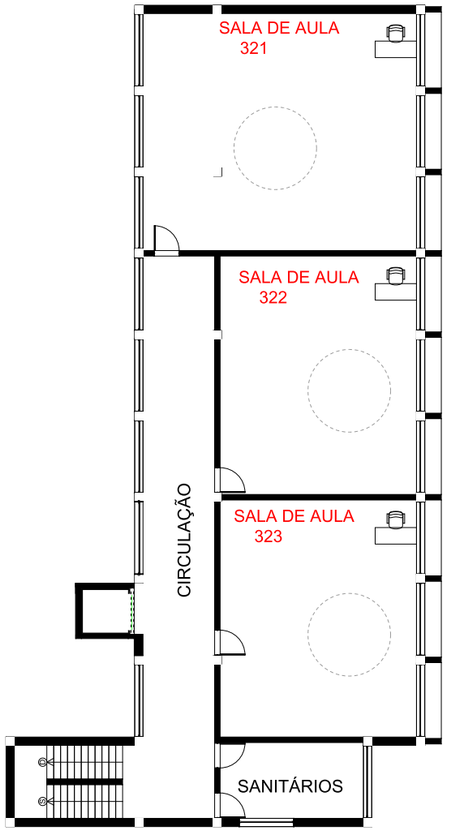

EDIFÍCIO 03 - 2º PAVIMENTO
PLANTA BAIXA
ESC.: 1 / 200

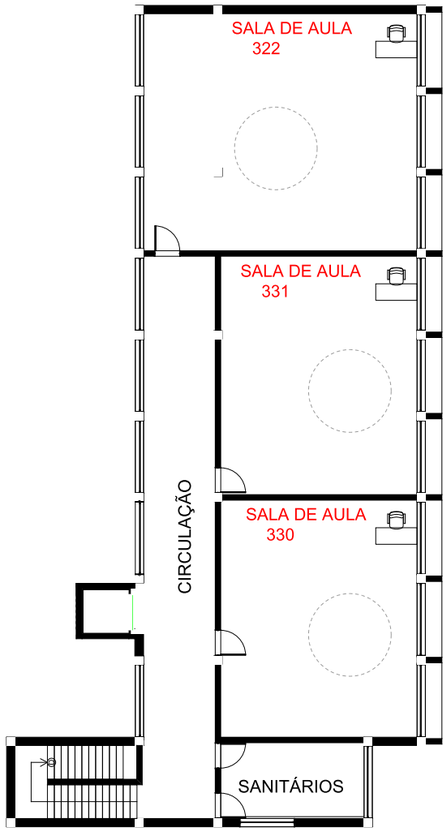

EDIFÍCIO 03 - 1º ANDAR
PLANTA BAIXA
ESC.: 1 / 200

0 m 10 m

Source: FUNDASP DIPLAD, MPCA_ARQ_Campus Marques_2024.11.06.dwg (sheets dated 25/11/2024). Converted with LibreDWG 0.14, rendered with ezdxf. Drawing units: metres.

Edifício 04 "Caio Prado"

Ground to 3rd floor; far right: ground-floor proposal (refectory, changing rooms, relocated window frames).




Source: FUNDASP DIPLAD, MPCA_ARQ_Campus Marques_2024.11.06.dwg (sheets dated 25/11/2024). Converted with LibreDWG 0.14, rendered with ezdxf. Drawing units: metres.

NUCC, maintenance and storage


NUCC (three levels: base, ground, upper), maintenance workshop and storage/kitchen annex.




NUCC
SUPERIOR

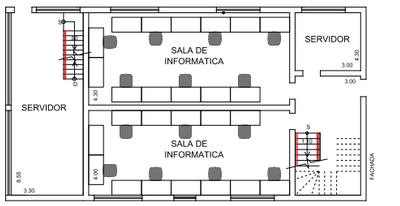


NUCC
TÉRREO

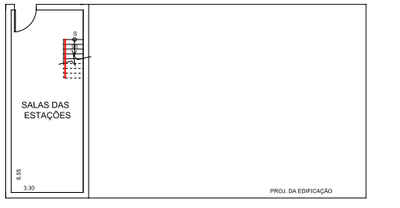

NUCC
EMBASAMENTO

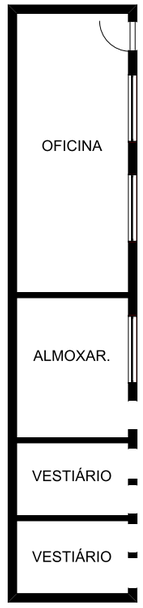

MANUTENÇÃO - TÉRREO
PLANTA BAIXA
ESC.: 1 / 125

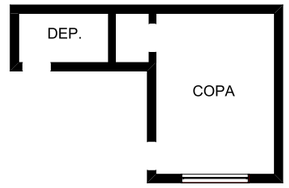

DEPÓSITO - TÉRREO
PLANTA BAIXA
ESC.: 1 / 125



Source: FUNDASP DIPLAD, MPCA_ARQ_Campus Marques_2024.11.06.dwg (sheets dated 25/11/2024). Converted with LibreDWG 0.14, rendered with ezdxf. Drawing units: metres.