PUC-SP Campus Consolação

Floor plans · Rua Marquês de Paranaguá 111, São Paulo · former Instituto Sedes Sapientiae (Rino Levi, 1940–42)

What this is

· The CAD set kept by FUNDASP's infrastructure division (DIPLAD) for the Marquês de Paranaguá campus, dated Nov 2024.

· It holds a site plan and room-level plans of every floor of Edifícios 01–04, plus NUCC, maintenance and storage.

· Its six print sheets are titled "Estudo COVID": a 2020-era distancing study (work stations in shifts A/B), updated in 2024.

· Earlier pages of this PDF are the CAD plans; the last pages are the historical and public sources gathered with them.

How far to trust it

· True scale, in metres: its 1.5 m distancing dimensions measure 1.500, and floor plans match the site plan (Edifício 01: 10.0 × 30.5 m vs 9.7 × 29.7 m).

· City GeoSampa footprints run 1–3 m larger (Edifício 01: 12.4 × 33.6 m): they trace roof edges from 1:5000 aerial survey, not walls.

· Current use, not the 1942 design: room names and numbers reflect 2020–2024 (e.g. Edifício 04 restaurant marked "desocupado").

· The campus note (1,600 students, 20 classrooms, 4 auditoriums, 20 IT labs) is dated 26/09/2014.

· No sections, heights or elevations. Floor-to-floor heights still come from LiDAR, photos and the Vitruvius section.

· Conversion losses: most layer names were dropped (colours kept), a few accented characters show as "?".

· Edifício 03's top floor is labelled "1º andar" in the file; its rooms are 330/331, so it is the 3rd floor.

Buildings and floors

· Edifício 01 (heritage core, ex-teaching block): ground, 1st, 2nd. Rooms 101–129D.

· Edifício 02 (long bar + auditorium): basement, ground, 1st, 2nd. Library and canteen below; rooms 201–226.

· Chapel: "Capela 36 lugares" beside the auditorium stage (Edifício 02 ground floor); the use-colour layer also marks room 204 as Capela.

· Edifício 03 (later): basement + 3 floors. Labs and data centre below; 3 classrooms per floor (311–331).

· Edifício 04 "Caio Prado" (later, on Rua Caio Prado): ground + 3 floors. Rooms 401–439.

· Also: NUCC (3 levels), maintenance workshop, storage/kitchen, guard houses, sports court, Casa Paroquial, Oficinas.

Heritage


· Condephaat SC 68/2010 and Conpresp 12/2015 protect Rino Levi's original core (1940–42):

· the auditorium block, the former dormitory, the teaching block and the inner patio. Later buildings are not protected.

Compiled 2026-10-19 by PUC Tech for the 3D campus map. Public and institutional sources only; see the last pages for credits.

Site plan

Rua Marquês de Paranaguá 111 (west) to Rua Caio Prado (east). Edifícios 01–04, auditorium, court, gardens, neighbours.

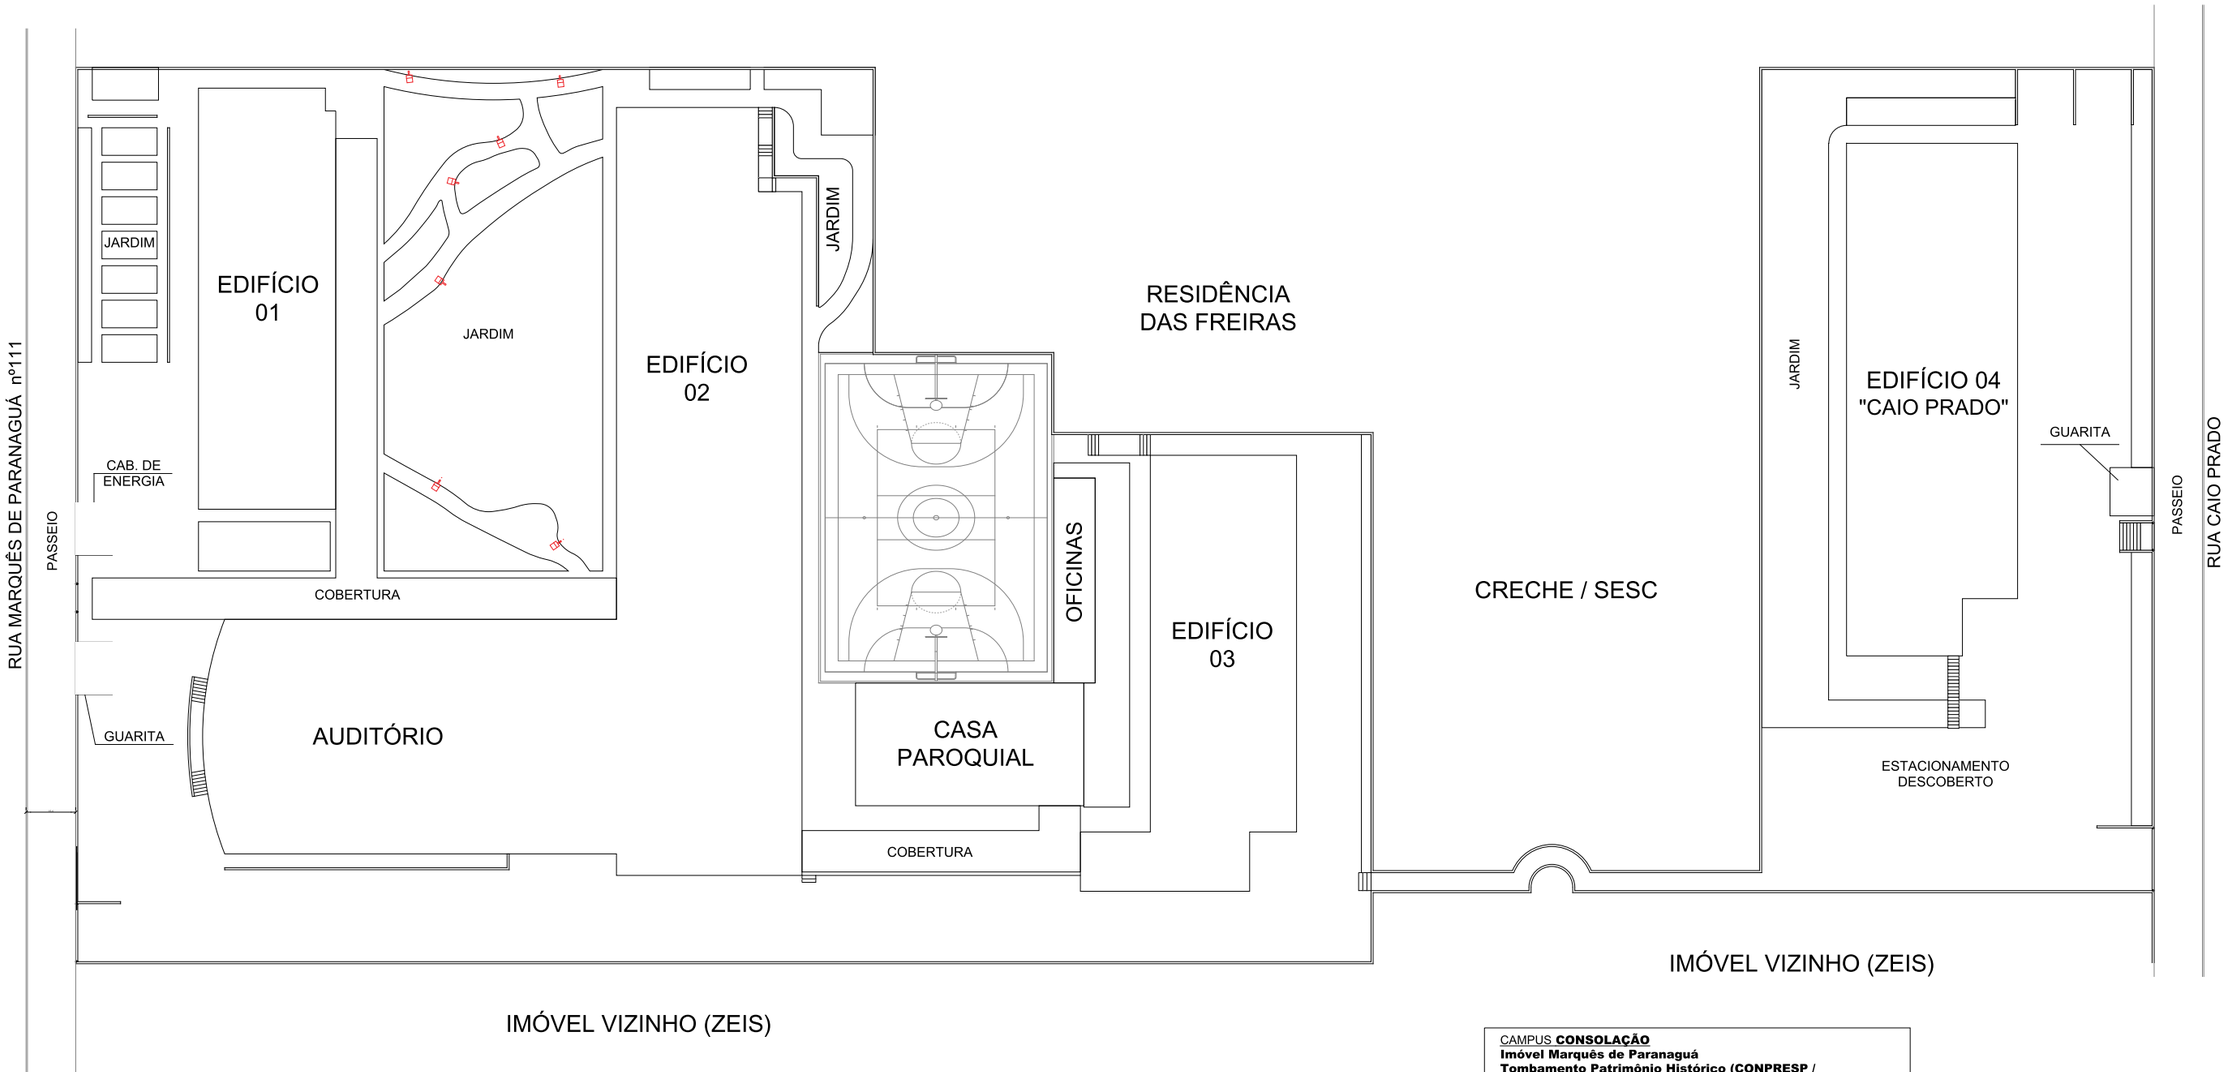


CAMPUS **CONSOLAÇÃO**
Imóvel Marquês de Paranaguá
Tombamento Patrimônio Histórico (CONPRESP / CONDEPHAAT)
- POPULAÇÃO FLUTUANTE TOTAL - 1600 alunos (em 26/09/2014)
- 20 SALAS DE AULA
- 04 AUDITÓRIOS
- 20 LABORATÓRIOS DE INFORMÁTICA
- LABORATÓRIOS TÉCNICOS

0 m — 20 m


Source: FUNDASP DIPLAD, MPCA_ARQ_Campus Marques_2024.11.06.dwg (sheets dated 25/11/2024). Converted with LibreDWG 0.14, rendered with ezdxf. Drawing units: metres.

Edifício 01


Ground, 1st and 2nd floors. Departments, coordinations, SAE, teachers' room, labs, postgraduate offices.

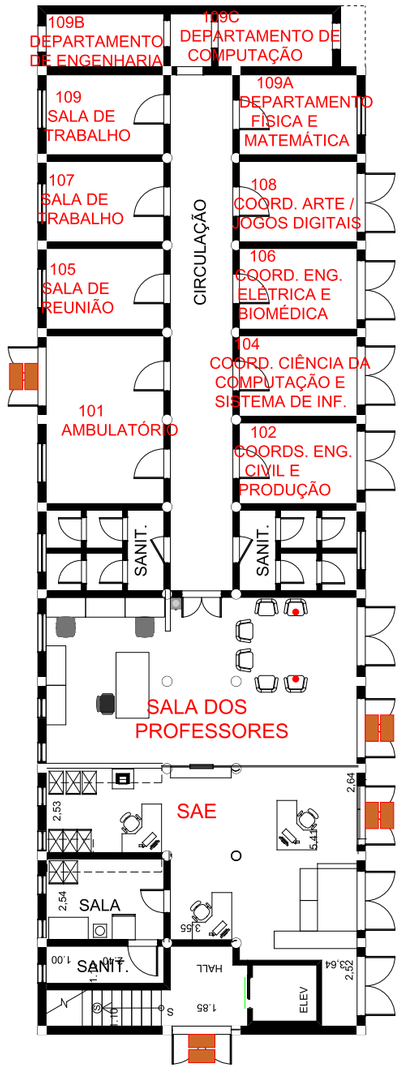

EDIFÍCIO 01 - TÉRREO
PLANTA BAIXA
ESC.: 1 / 200

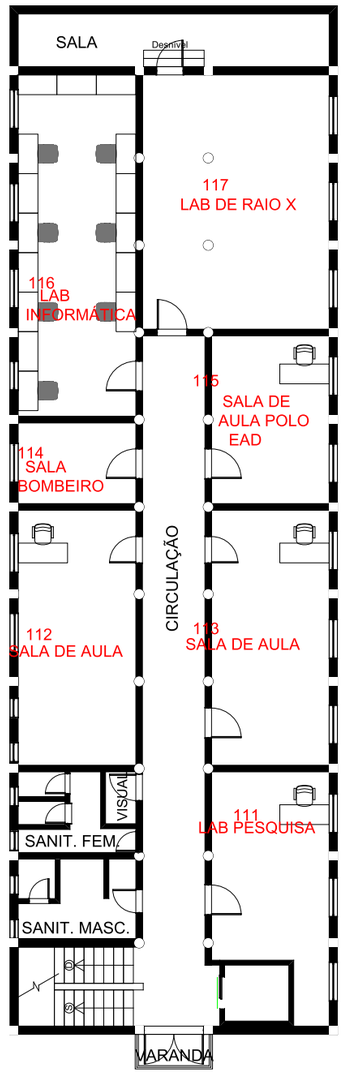

EDIFÍCIO 01 - 1º ANDAR
PLANTA BAIXA
ESC.: 1 / 200

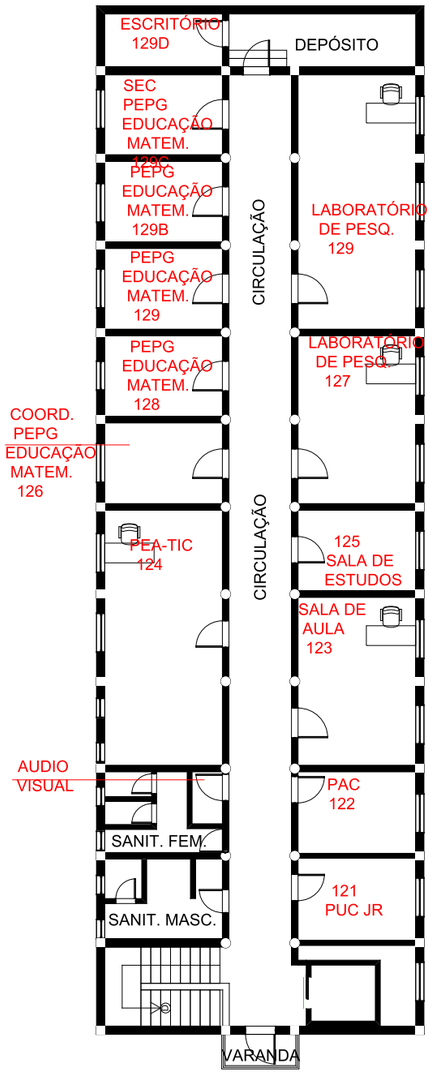


EDIFÍCIO 01 - 2º ANDAR
PLANTA BAIXA
ESC.: 1 / 200


0 m 5 m

Edifício 02


Basement (library, canteen), ground (auditorium, chapel, classrooms), 1st (direction, IT labs), 2nd (engineering labs). Fills mark room use: robotics lab (green), chapel (magenta), IT labs (grey).

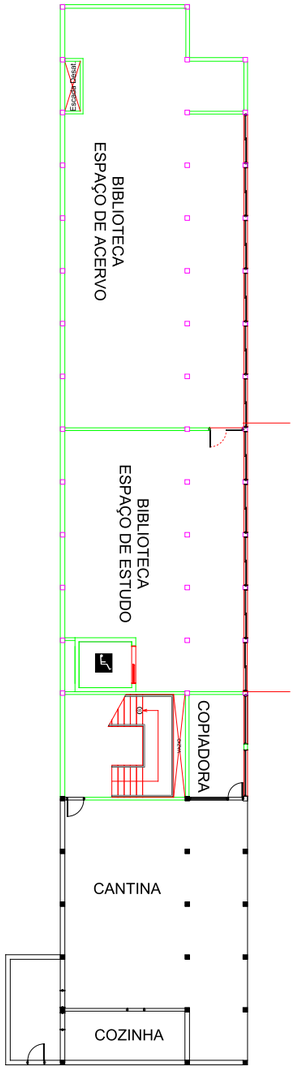


EDIFÍCIO 02 - SUBSOLO
PLANTA BAIXA
ESCALA: 1 / 300

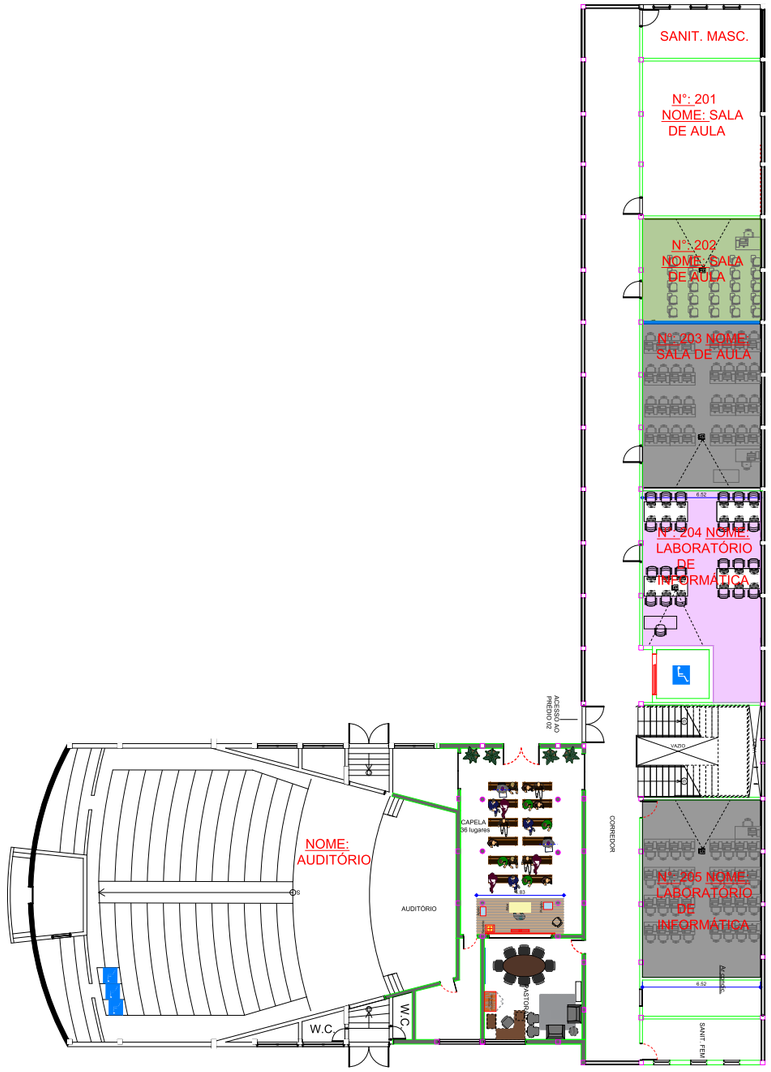

EDIFÍCIO 02 - TÉRREO
PLANTA BAIXA
ESCALA: 1 / 300

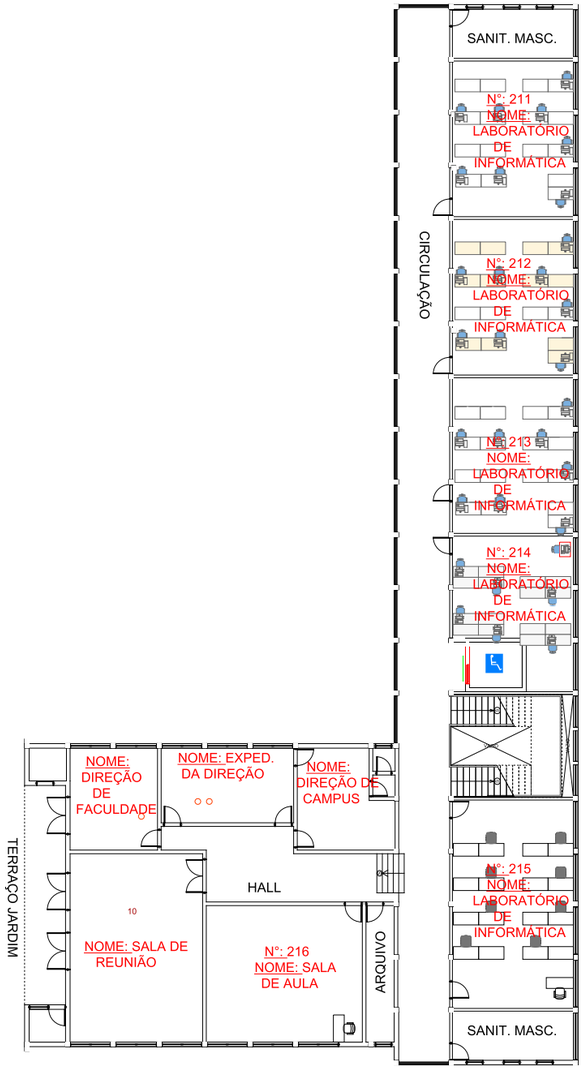

EDIFÍCIO 02 - 1º ANDAR
PLANTA BAIXA
ESCALA: 1 / 300

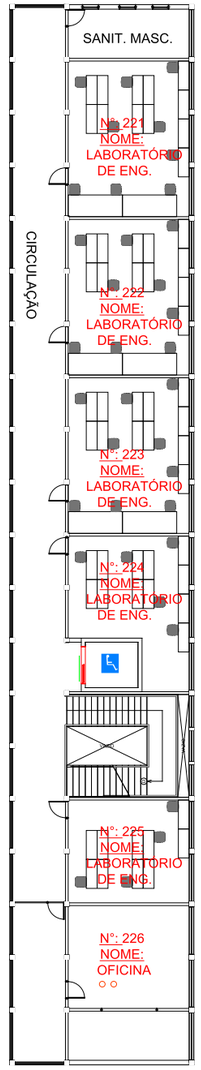


EDIFÍCIO 02 - 2º ANDAR
PLANTA BAIXA
ESCALA: 1 / 300

0 m 10 m


Source: FUNDASP DIPLAD, MPCA_ARQ_Campus Marques_2024.11.06.dwg (sheets dated 25/11/2024). Converted with LibreDWG 0.14, rendered with ezdxf. Drawing units: metres.

Edifício 03


Basement (mechanics/fluids labs, data centre; proposed layout) and three classroom floors (311–313, 321–323, 330–331).

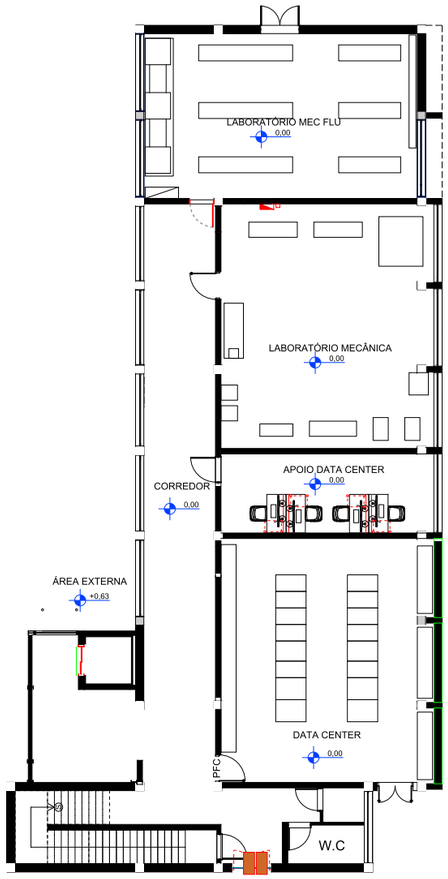


EDIFÍCIO 03 - SUBSOLO
PLANTA BAIXA - LAYOUT PROPOSTO
ESC.: 1 / 200

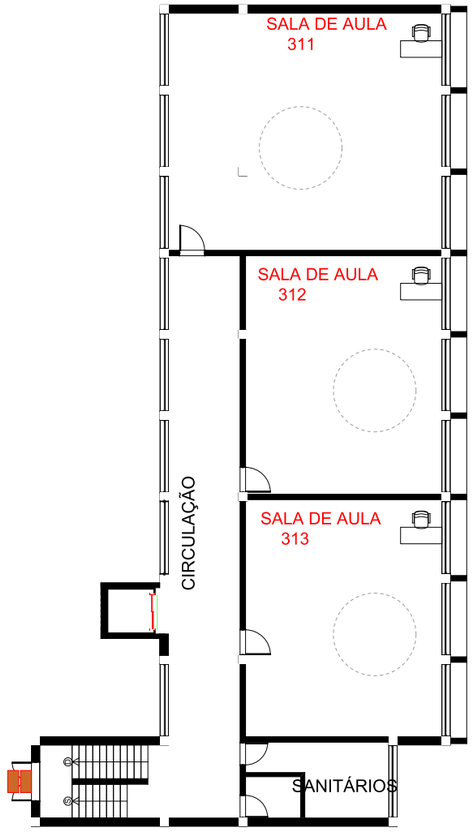

EDIFÍCIO 03 - 1º PAVIMENTO
PLANTA BAIXA
ESC.: 1 / 200

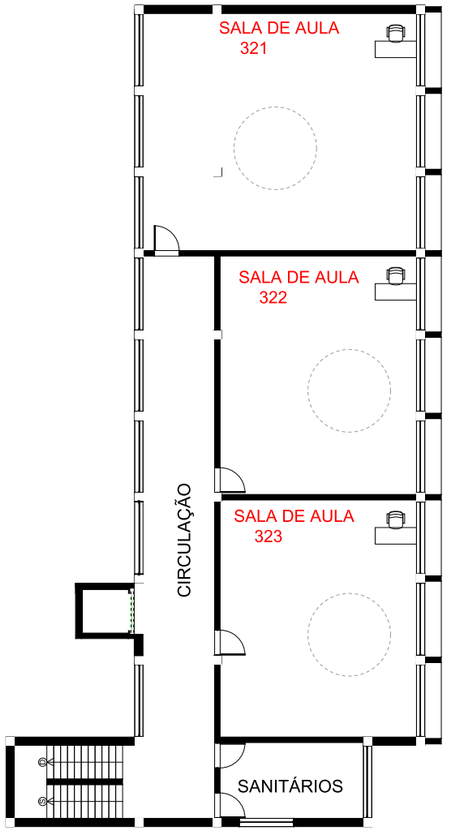

EDIFÍCIO 03 - 2° PAVIMENTO
PLANTA BAIXA
ESC.: 1 / 200

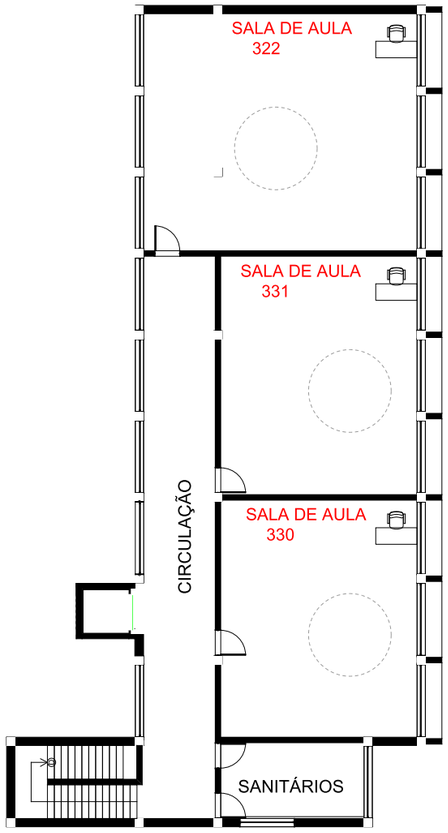


EDIFÍCIO 03 - 1º ANDAR
PLANTA BAIXA
ESC.: 1 / 200

0 m 10 m

Source: FUNDASP DIPLAD, MPCA_ARQ_Campus Marques_2024.11.06.dwg (sheets dated 25/11/2024). Converted with LibreDWG 0.14, rendered with ezdxf. Drawing units: metres.

Edifício 04 "Caio Prado"

Ground to 3rd floor; far right: ground-floor proposal (refectory, changing rooms, relocated window frames).

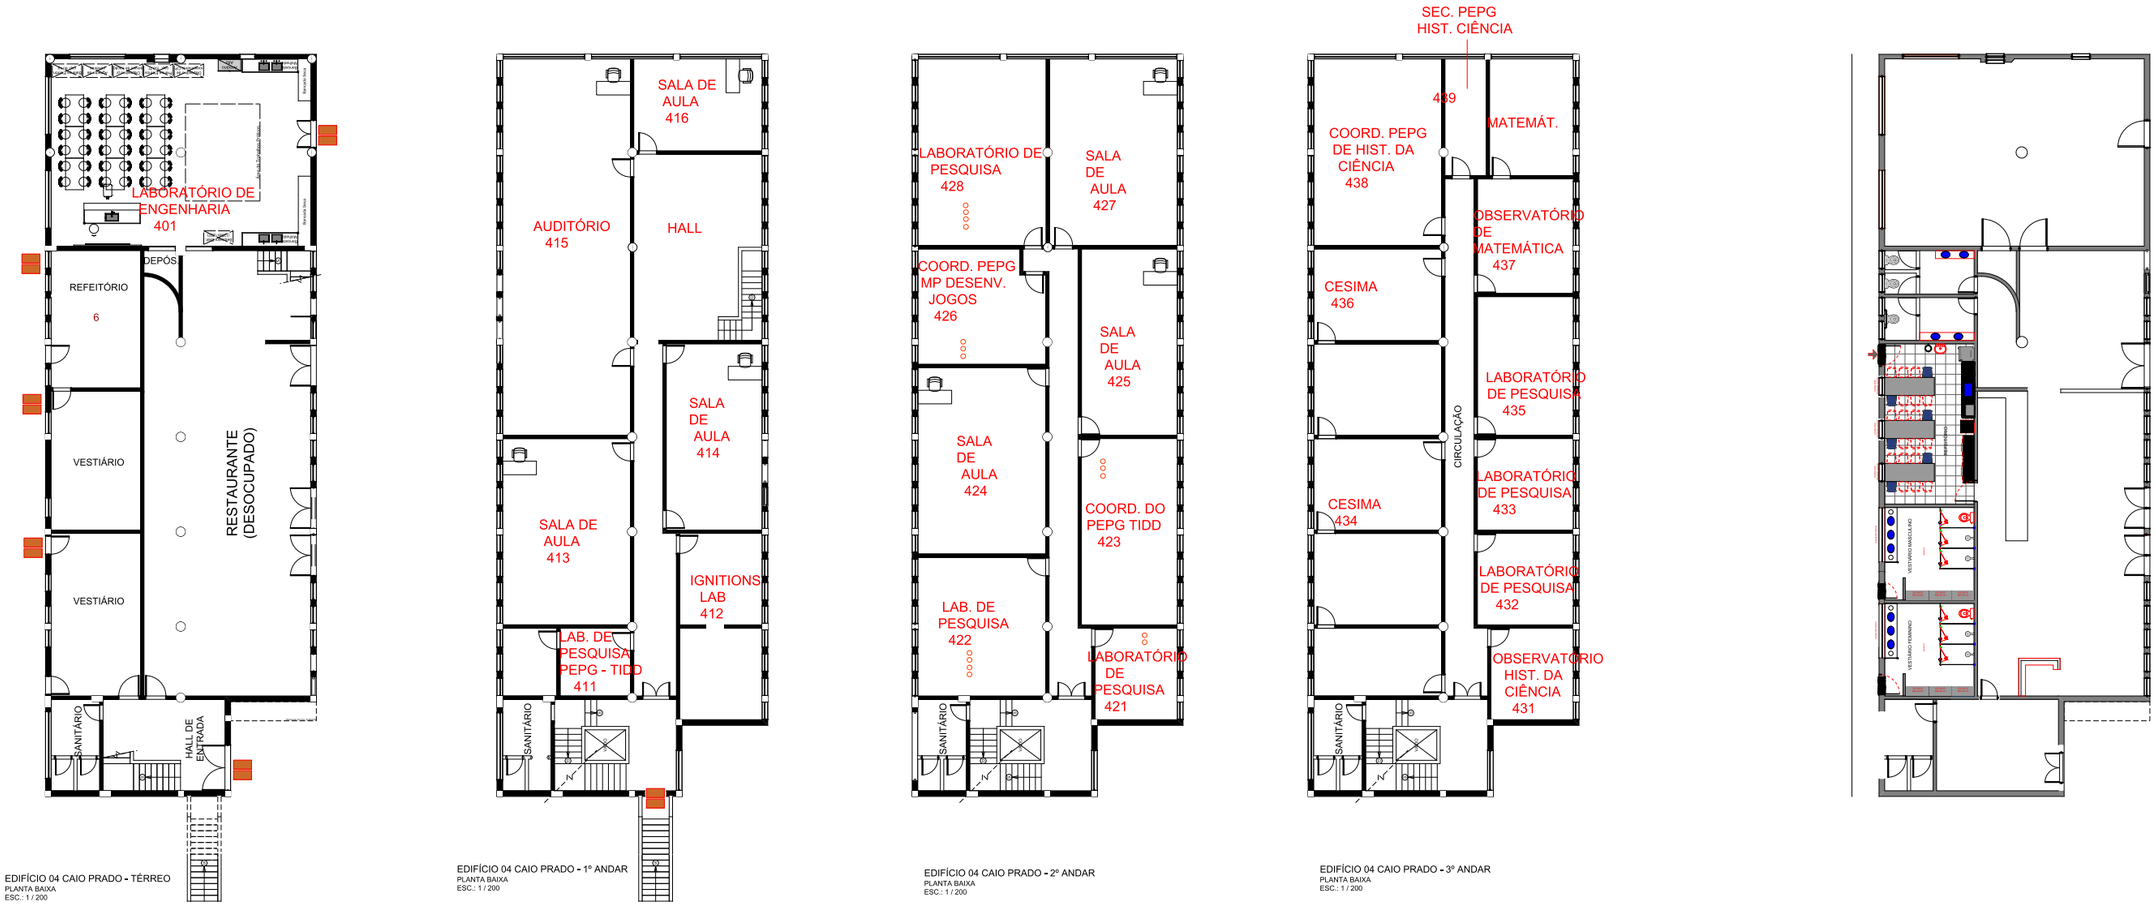


Source: FUNDASP DIPLAD, MPCA_ARQ_Campus Marques_2024.11.06.dwg (sheets dated 25/11/2024). Converted with LibreDWG 0.14, rendered with ezdxf. Drawing units: metres.

NUCC, maintenance and storage


NUCC (three levels: base, ground, upper), maintenance workshop and storage/kitchen annex.




NUCC
SUPERIOR

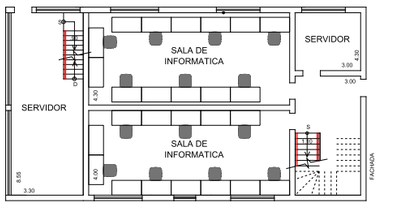


NUCC
TÉRREO

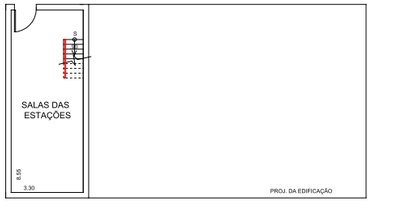

NUCC
EMBASAMENTO

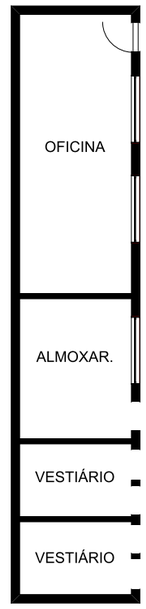

MANUTENÇÃO - TÉRREO
PLANTA BAIXA
ESC.: 1 / 125

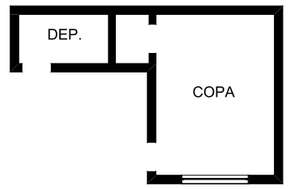


DEPÓSITO - TÉRREO
PLANTA BAIXA
ESC.: 1 / 125

0 m 10 m

Source: FUNDASP DIPLAD, MPCA_ARQ_Campus Marques_2024.11.06.dwg (sheets dated 25/11/2024). Converted with LibreDWG 0.14, rendered with ezdxf. Drawing units: metres.

Original design: ground floor


Rino Levi's Instituto Sedes Sapientiae (1940–42), redrawn by Ana Paula Koury. Low resolution (528 × 344 px).

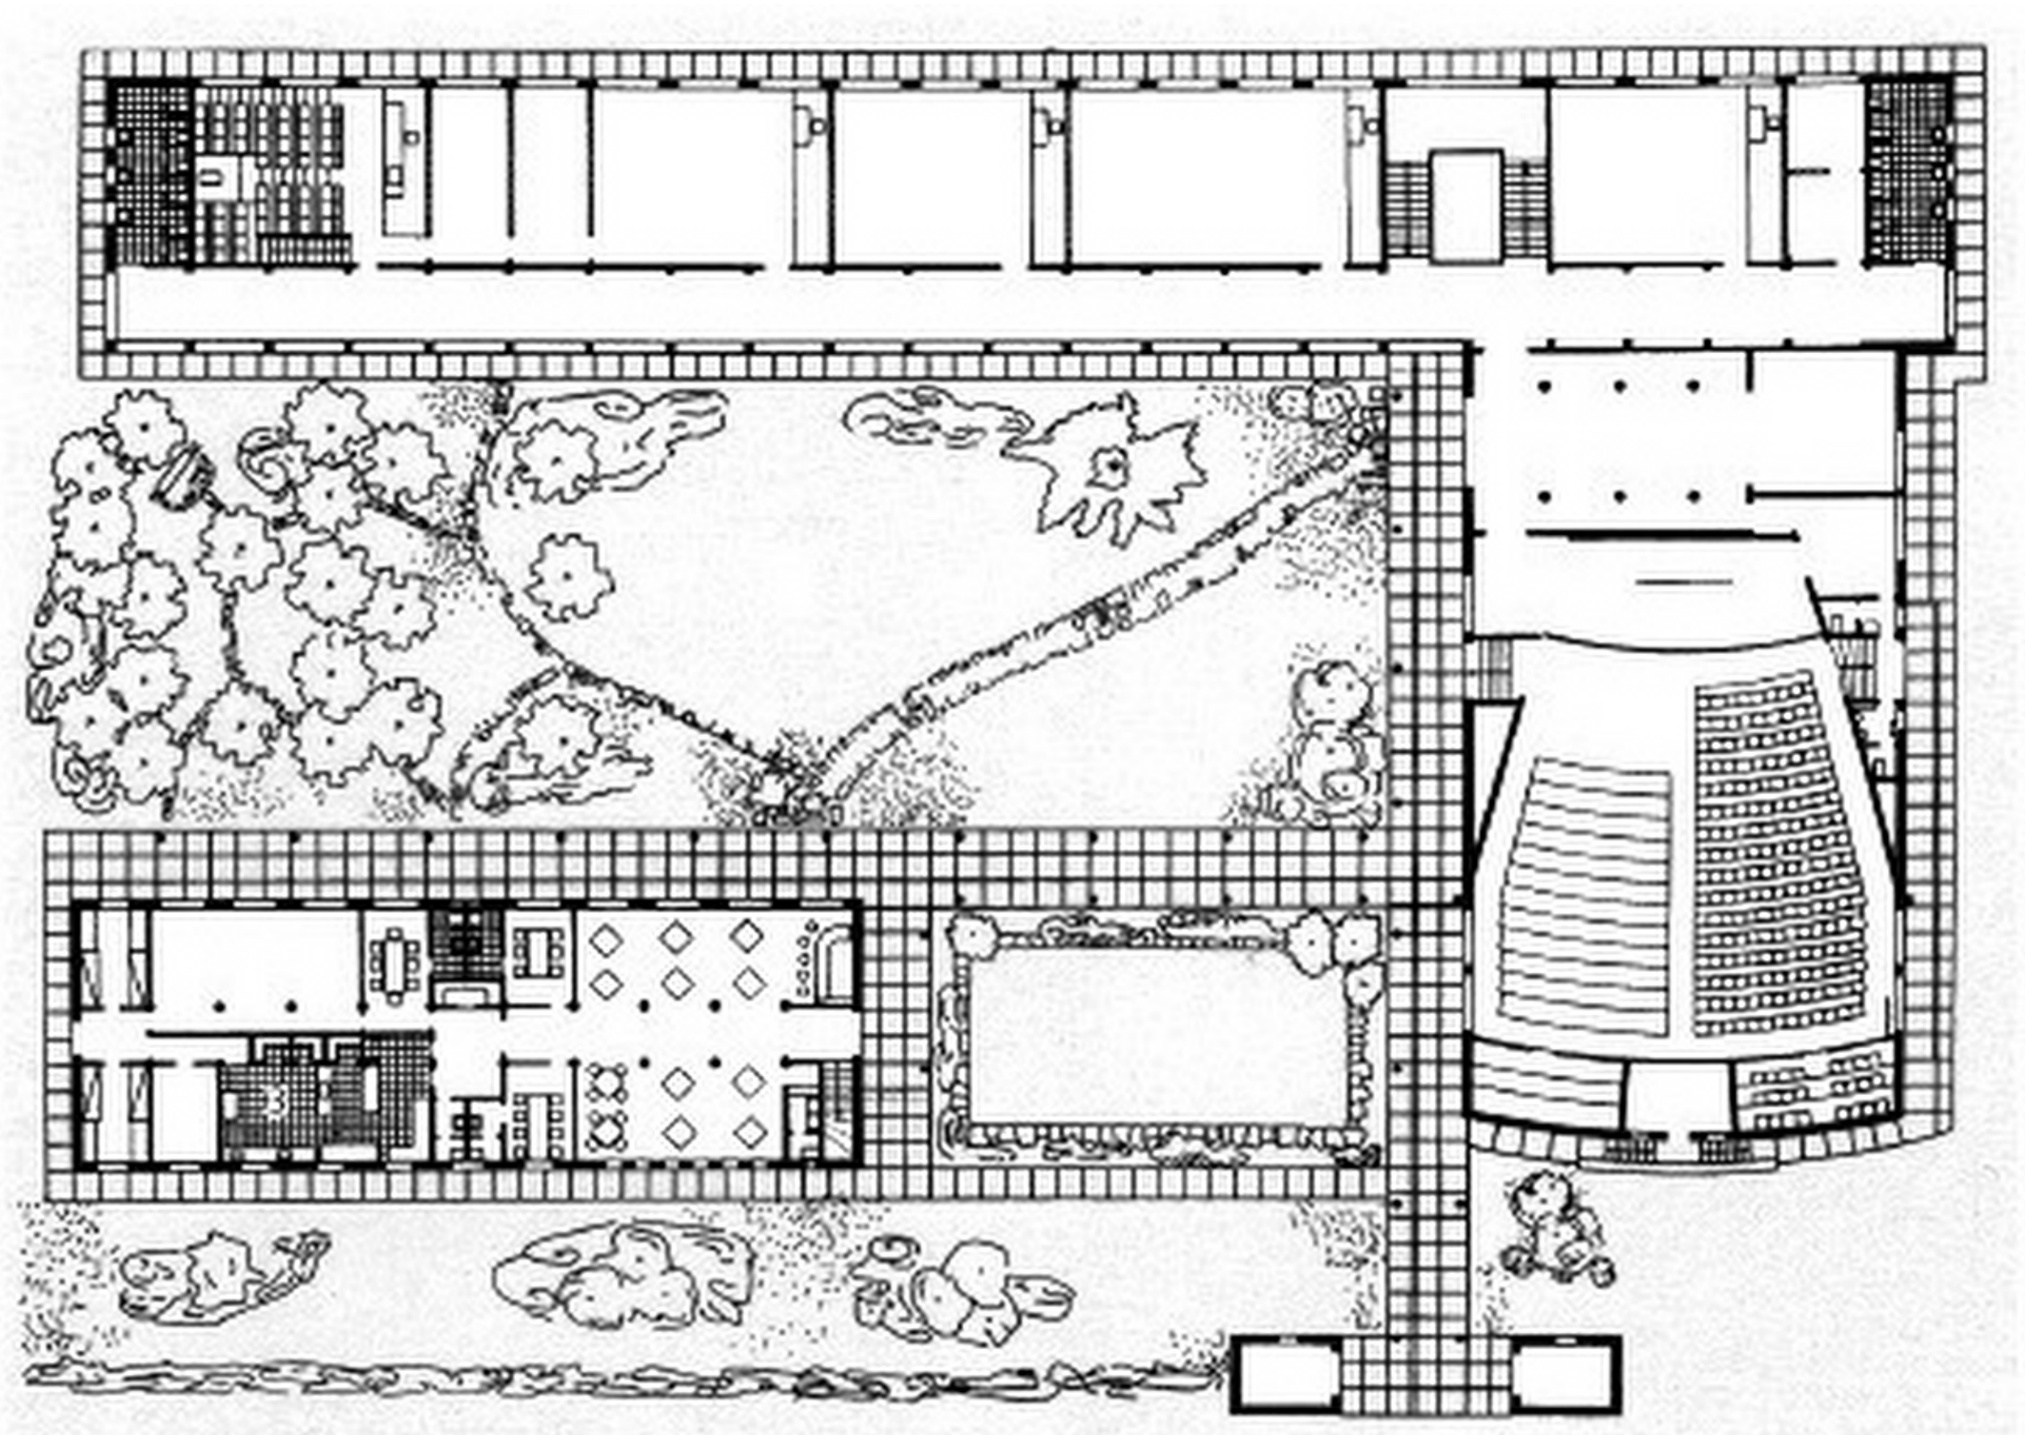

Source: Vitruvius, Minha Cidade 18.216 · vitruvius.com.br/revistas/read/minhacidade/18.216/7066

Original design: upper floor


Classroom bar, auditorium wing with roof garden, dormitory block. Same redrawing.

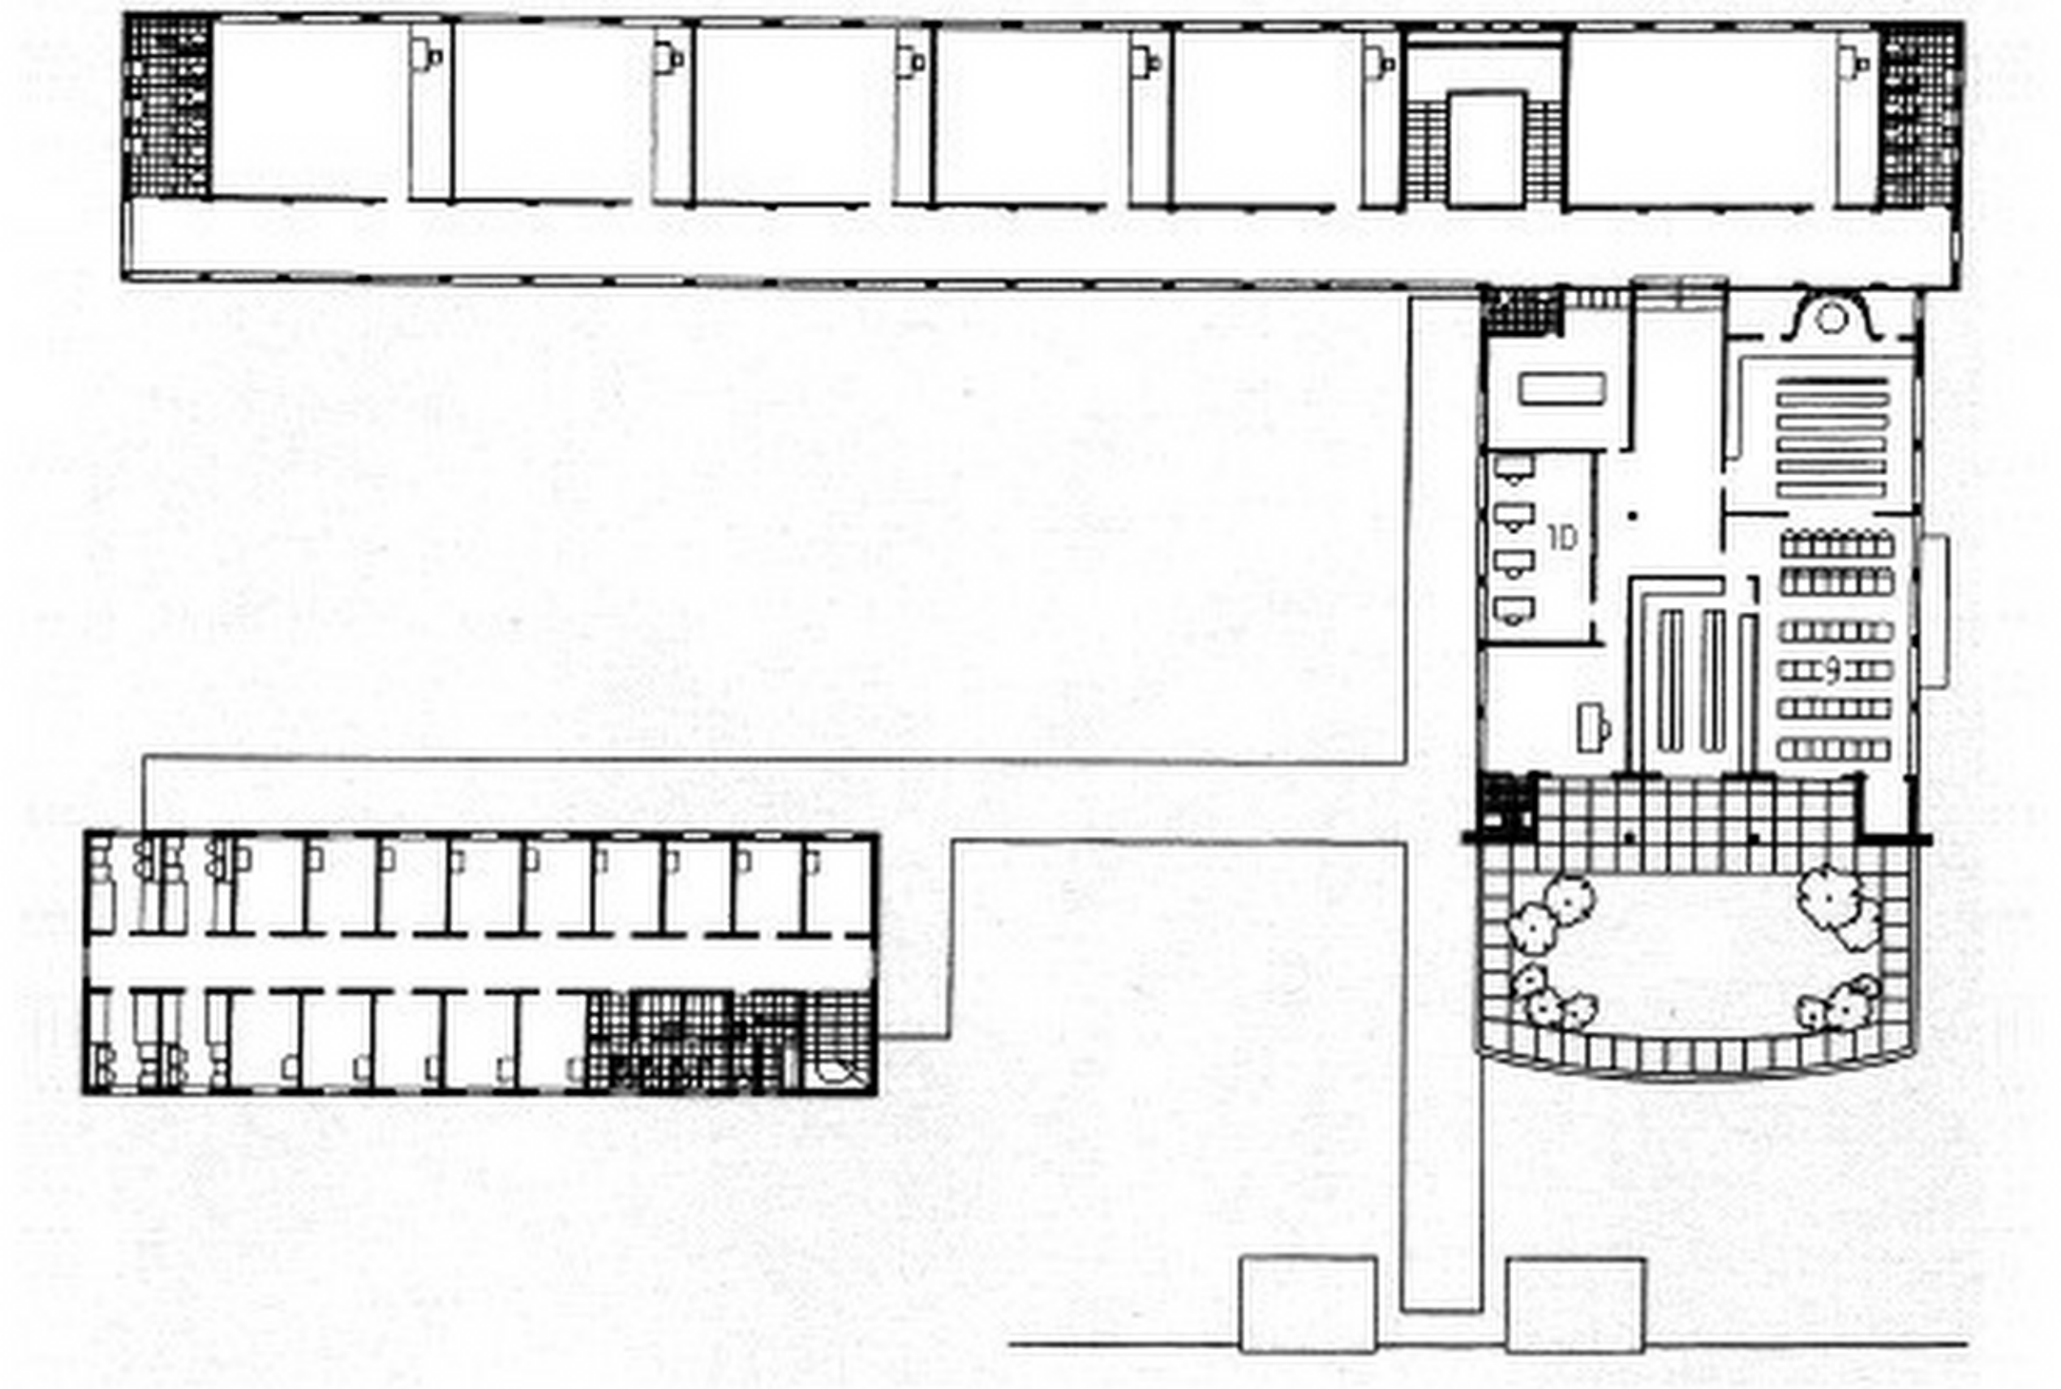

Source: Vitruvius, Minha Cidade 18.216 · vitruvius.com.br/revistas/read/minhacidade/18.216/7066

Classroom block: section and west elevation

Cobogó screen: 0.28 m modules, 4.00 m floor to floor (0.60 + 0.84 + 2.54 m). Scales 1:100 and 1:25.

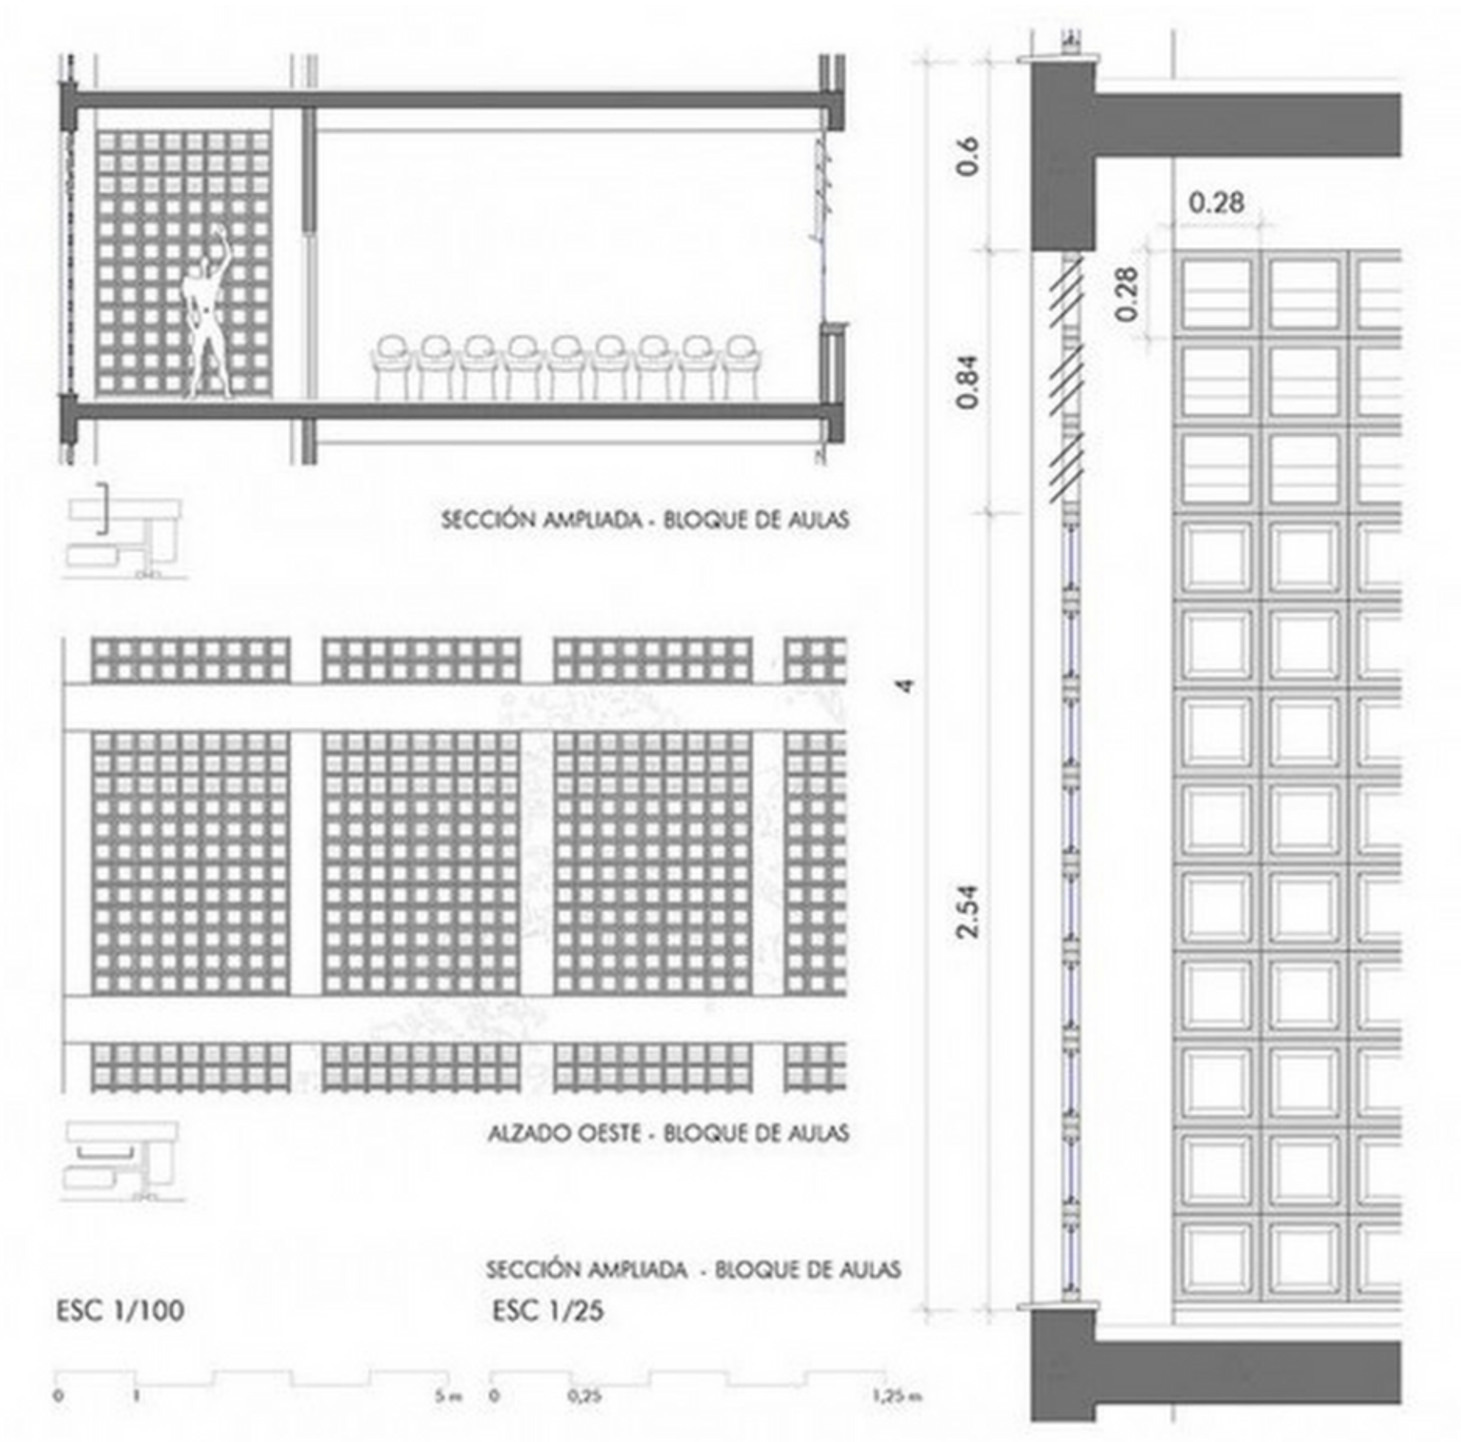

Source: Vitruvius, Arquitextos 21.249 · vitruvius.com.br/revistas/read/arquitextos/21.249/8012

PUC-SP campus map

Official footprints only, no rooms.



Source: PUC-SP PUC Tour · www5.pucsp.br/puc-tour/consolacao.php